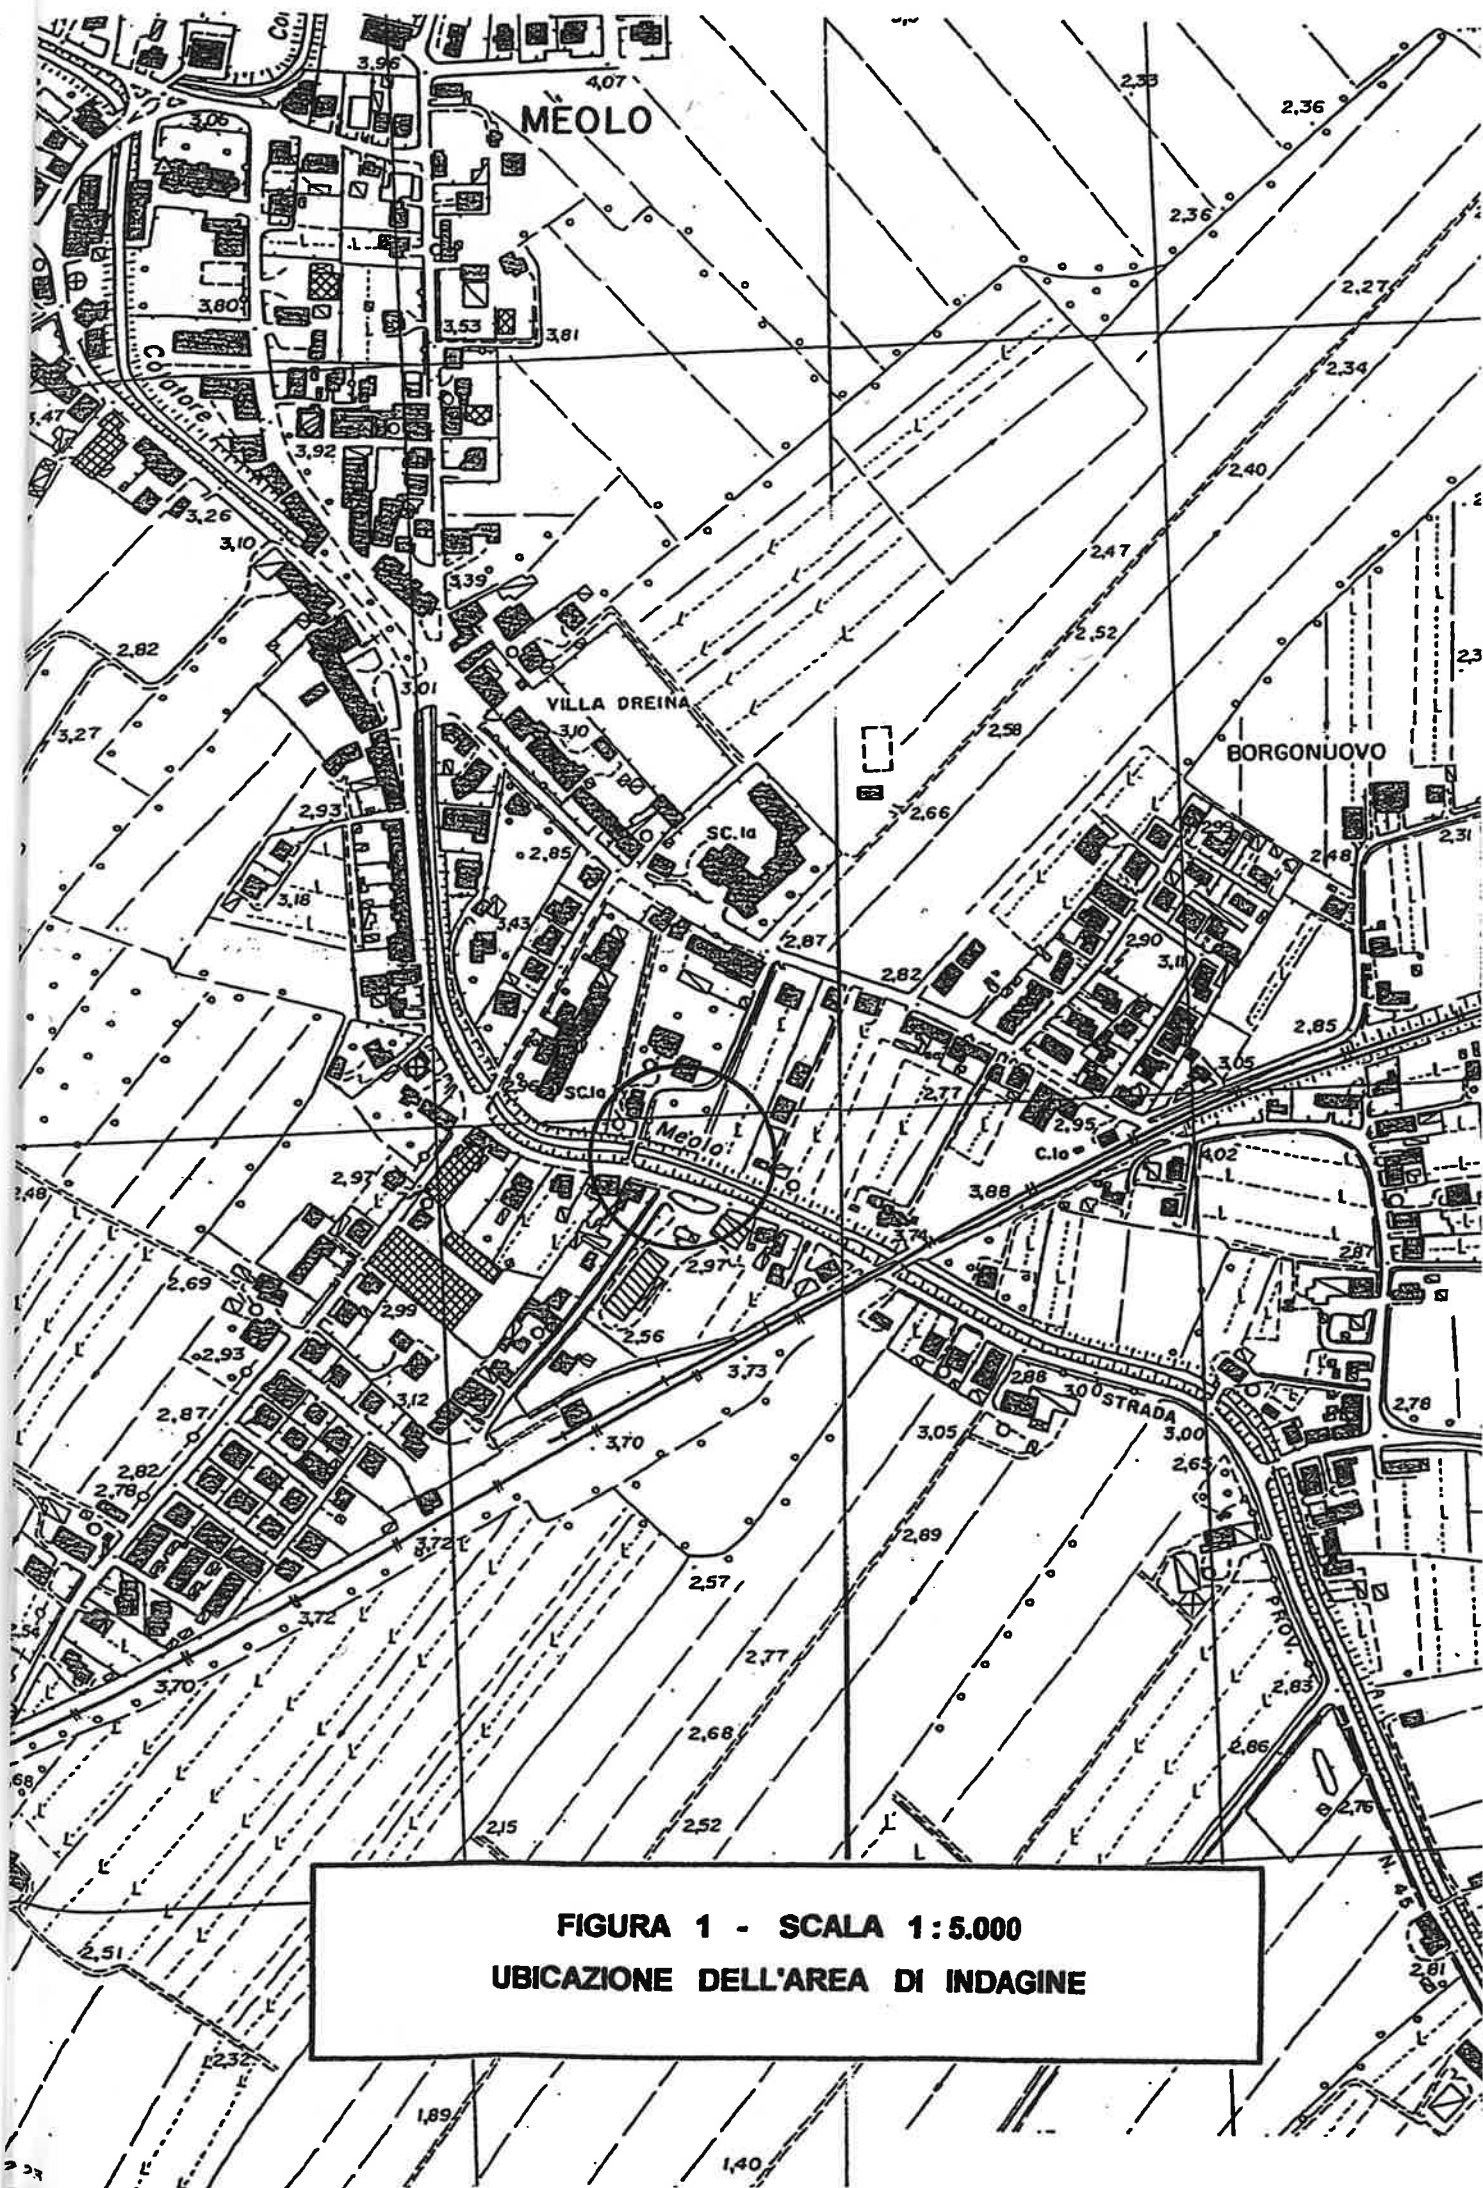




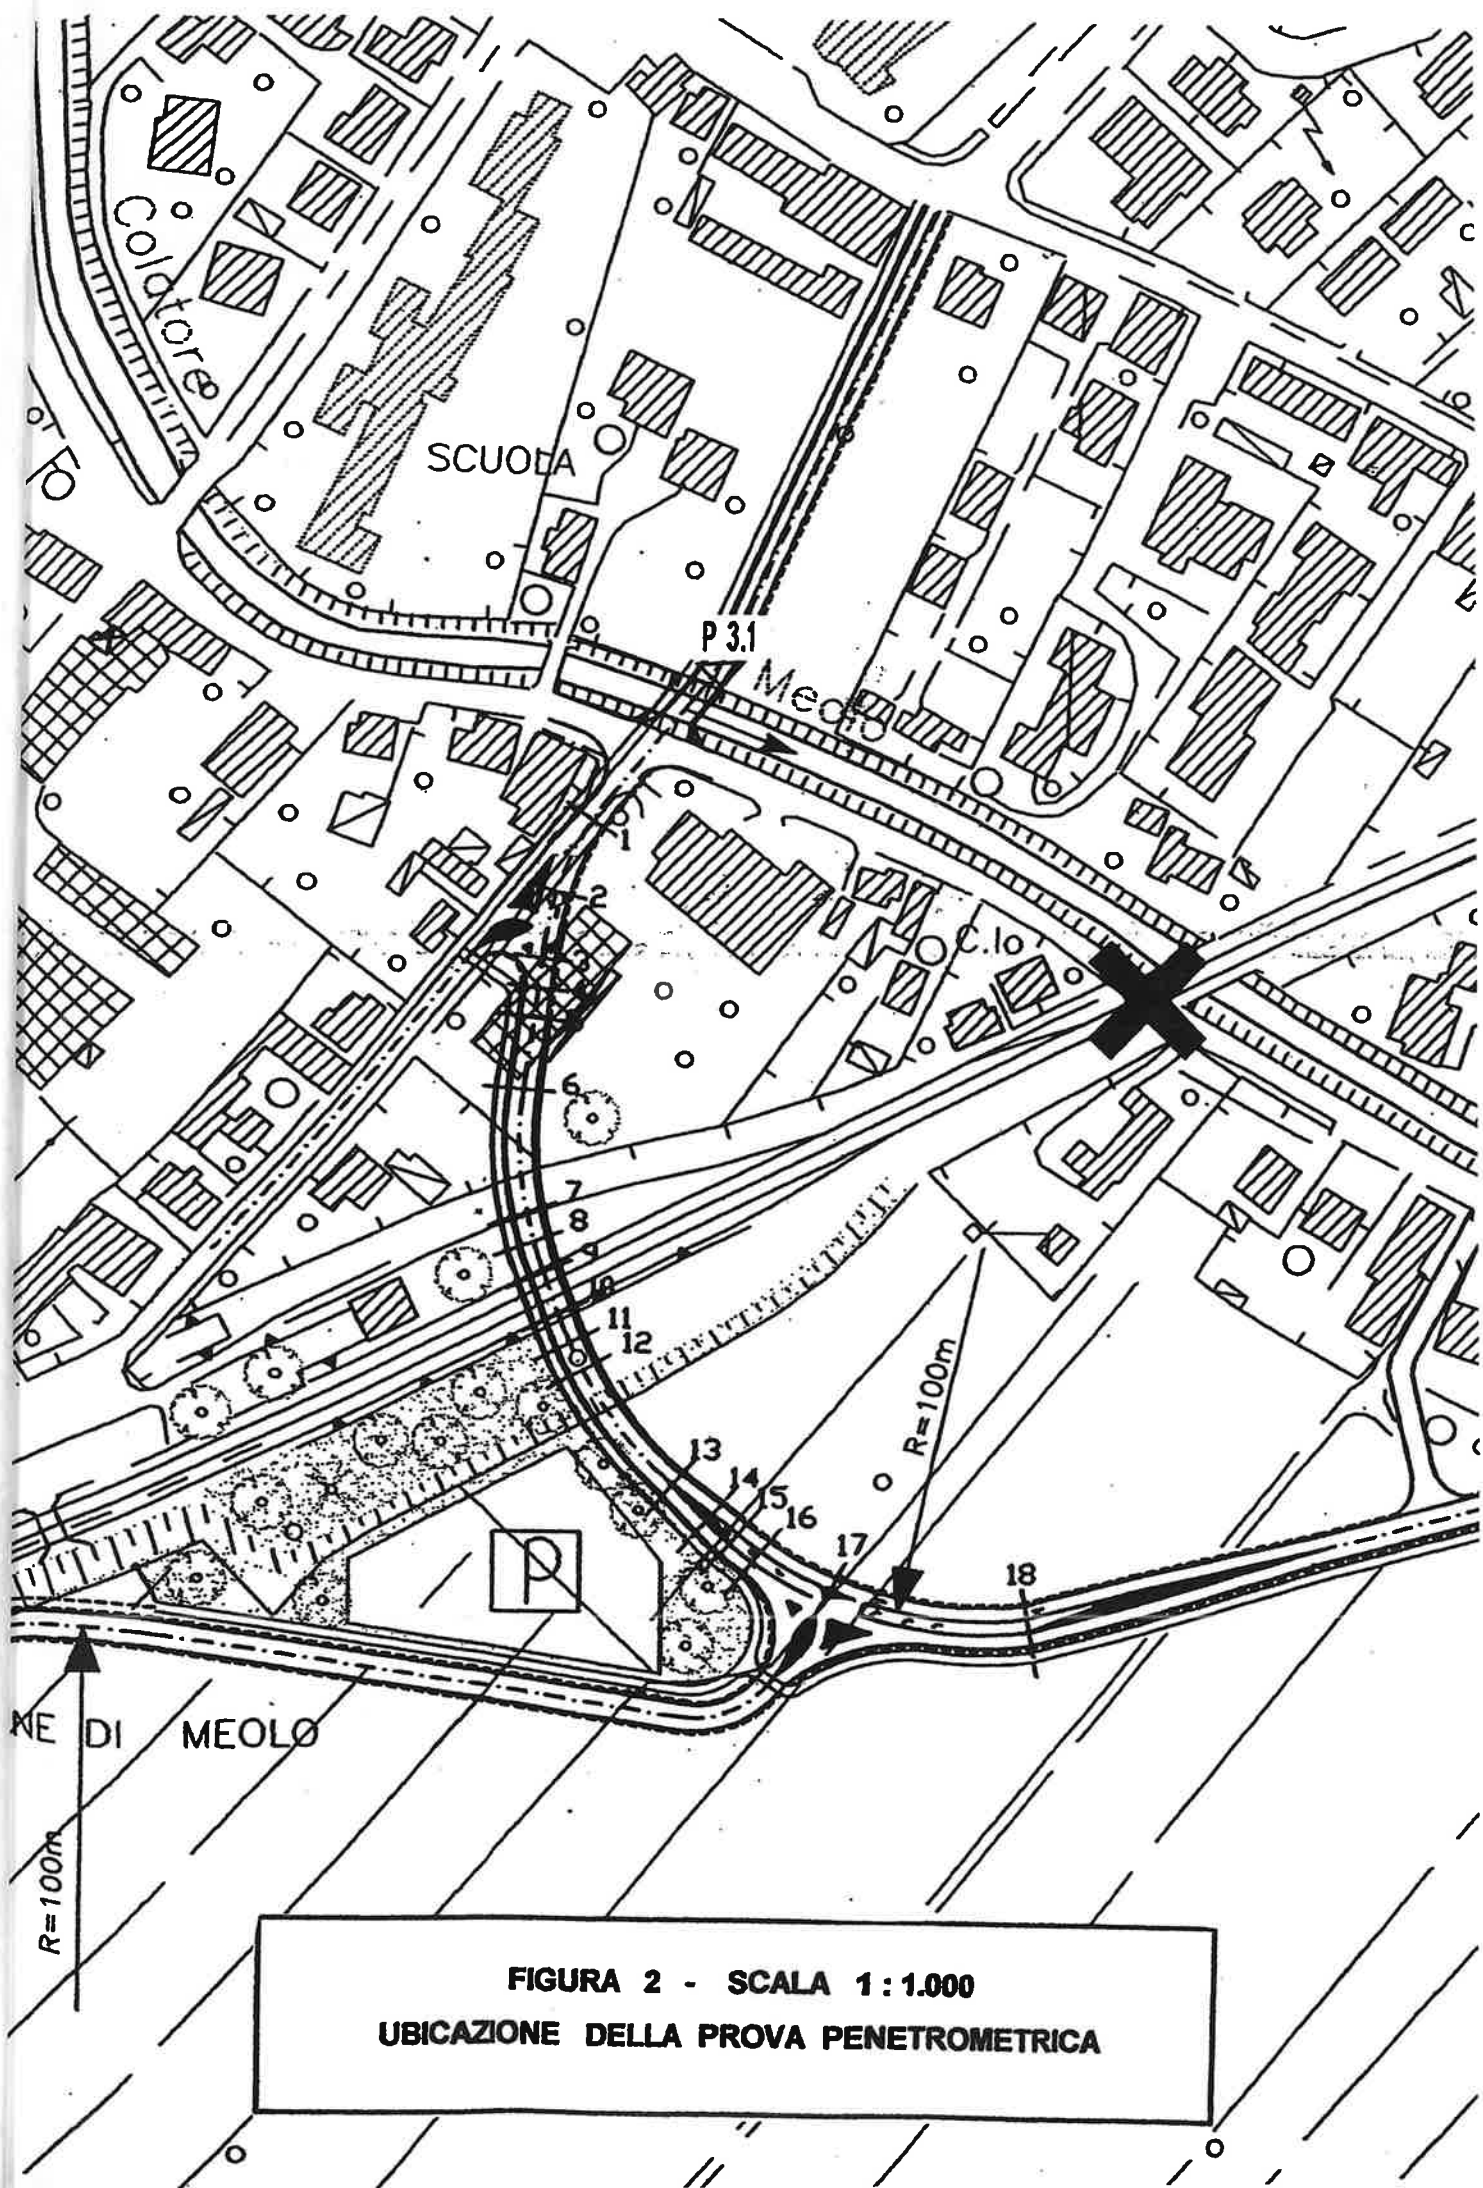


FIGURA 2 - SCALA 1:1.000
UBICAZIONE DELLA PROVA PENETROMETRICA



GEOSERVIZI S.R.L.

Via Roma, 54

31020 VILLORBA (TV)

Tel. 0422/918445 Fax 0422/918640

COMMITTENTE: DOTT. ING. FLAVIO ZANCHETTIN

CANTIERE: MELO

PENETROMETRIA: P3.1

DATA: 15/09/99 QUOTA: -0.60 m DA P 3.3



RAPPORTO R_p/R_1 (BEGEMANN)

PENETROMETRO STATICO olandese da 20 tonnellate

16 32 60 100
A AL LS SL S GS

R1 : ATTRITO LATERALE LOCALE (Kg/cmq)

Rp : RESISTENZA ALLA PUNTA (Kg/cmq)

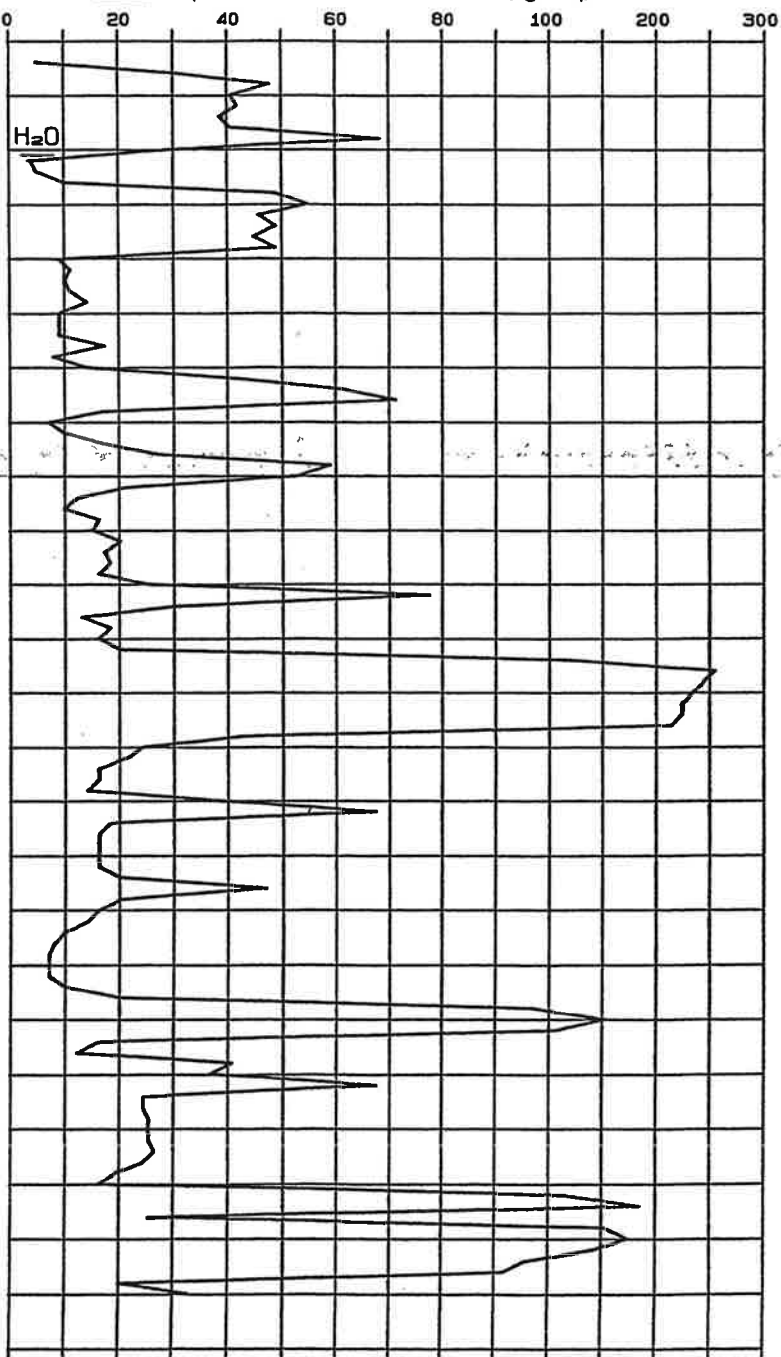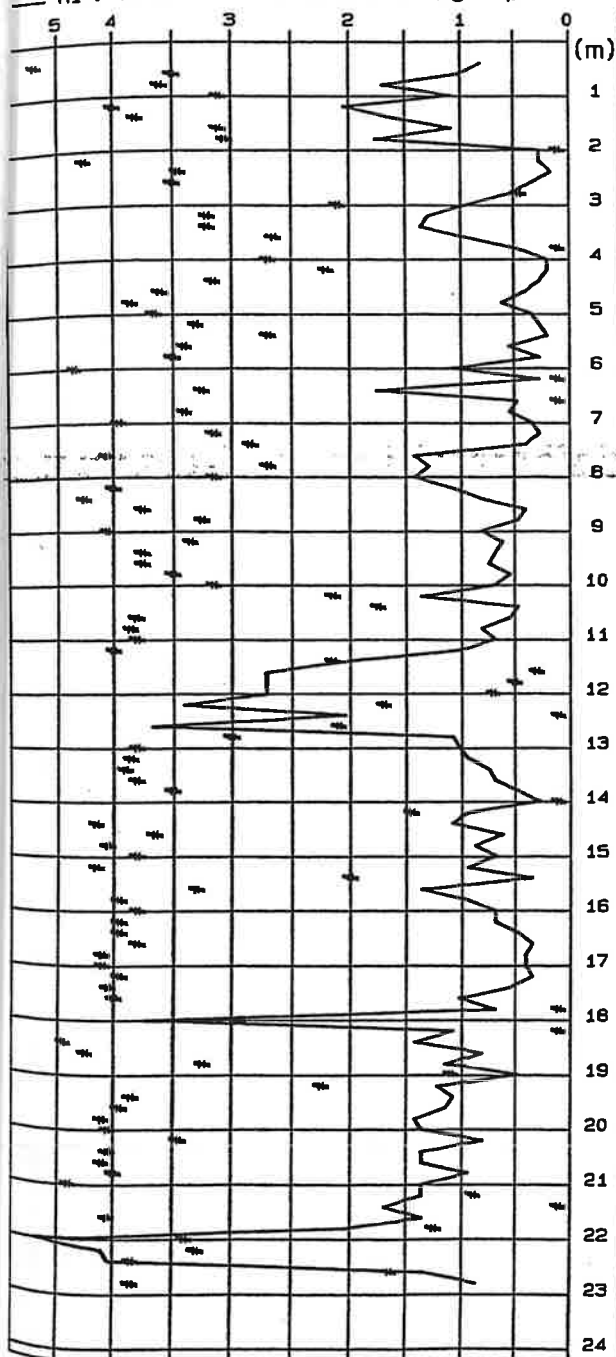

MODELLO GEOTECNICO DEL TERRENO

Penetrometria di riferimento : P3.1

Cantiere : NEOLO

Data : 15/09/99
Quota zero : P.C.

QUOTE DELLO STRATO (m)	SPESSORE (cm)	INTERPRETAZIONE STRATIGRAFICA	Rp media (kg/cm ²)	RL media (kg/cm ²)	E' (kg/cm ²)	Phi' (gradi)	Cu (kg/cm ²)
-0.40 -2.10	170	LIMO ARGILLOSO	38	1.27	73.37	0	1.90
-2.10 -2.70	60	ARGILLA LIMOSA	6	0.26	24.30	0	0.30
-2.70 -3.90	120	LIMO SABBIOSO	48	0.93	97.43	34	0.00
-3.90 -6.10	220	ARGILLA LIMOSA	11	0.40	45.95	0	0.55
-6.10 -6.70	60	SABBIA E LIMO	57	0.83	103.52	35	0.00
-6.70 -7.70	100	ARGILLA LIMOSA	15	0.59	52.80	0	0.75
-7.70 -8.10	40	SABBIA E LIMO	56	1.36	112.10	35	0.00
-8.10 -10.10	200	ARGILLA LIMOSA	17	0.68	55.98	0	0.85
-10.10 -10.50	40	SABBIA LIMOSA	54	0.92	108.00	35	0.00
-10.50 -11.30	80	ARGILLA LIMOSA	17	0.76	56.68	0	0.85
-11.30 -12.70	140	SABBIA LIMOSA	216	2.76	332.80	44	0.00
-12.70 -15.90	320	ARGILLA LIMOSA CON INTERCALAZ. DI LIMO SABBIOSO	25	0.81	66.80	0	1.25
-15.90 -17.70	180	ARGILLA DEBOLMENTE LIMOSA	11	0.54	39.55	0	0.55
-17.70 -19.30	160	SABBIA LIMOSA CON INTERCALAZ. ARGILLOSA	66	1.32	126.86	36	0.00
-19.30 -21.10	180	ARGILLA DEBOLMENTE LIMOSA	23	1.21	50.73	0	1.15
-21.10 -23.00	190	SABBIA LIMOSA	103	2.24	178.47	38	0.00