

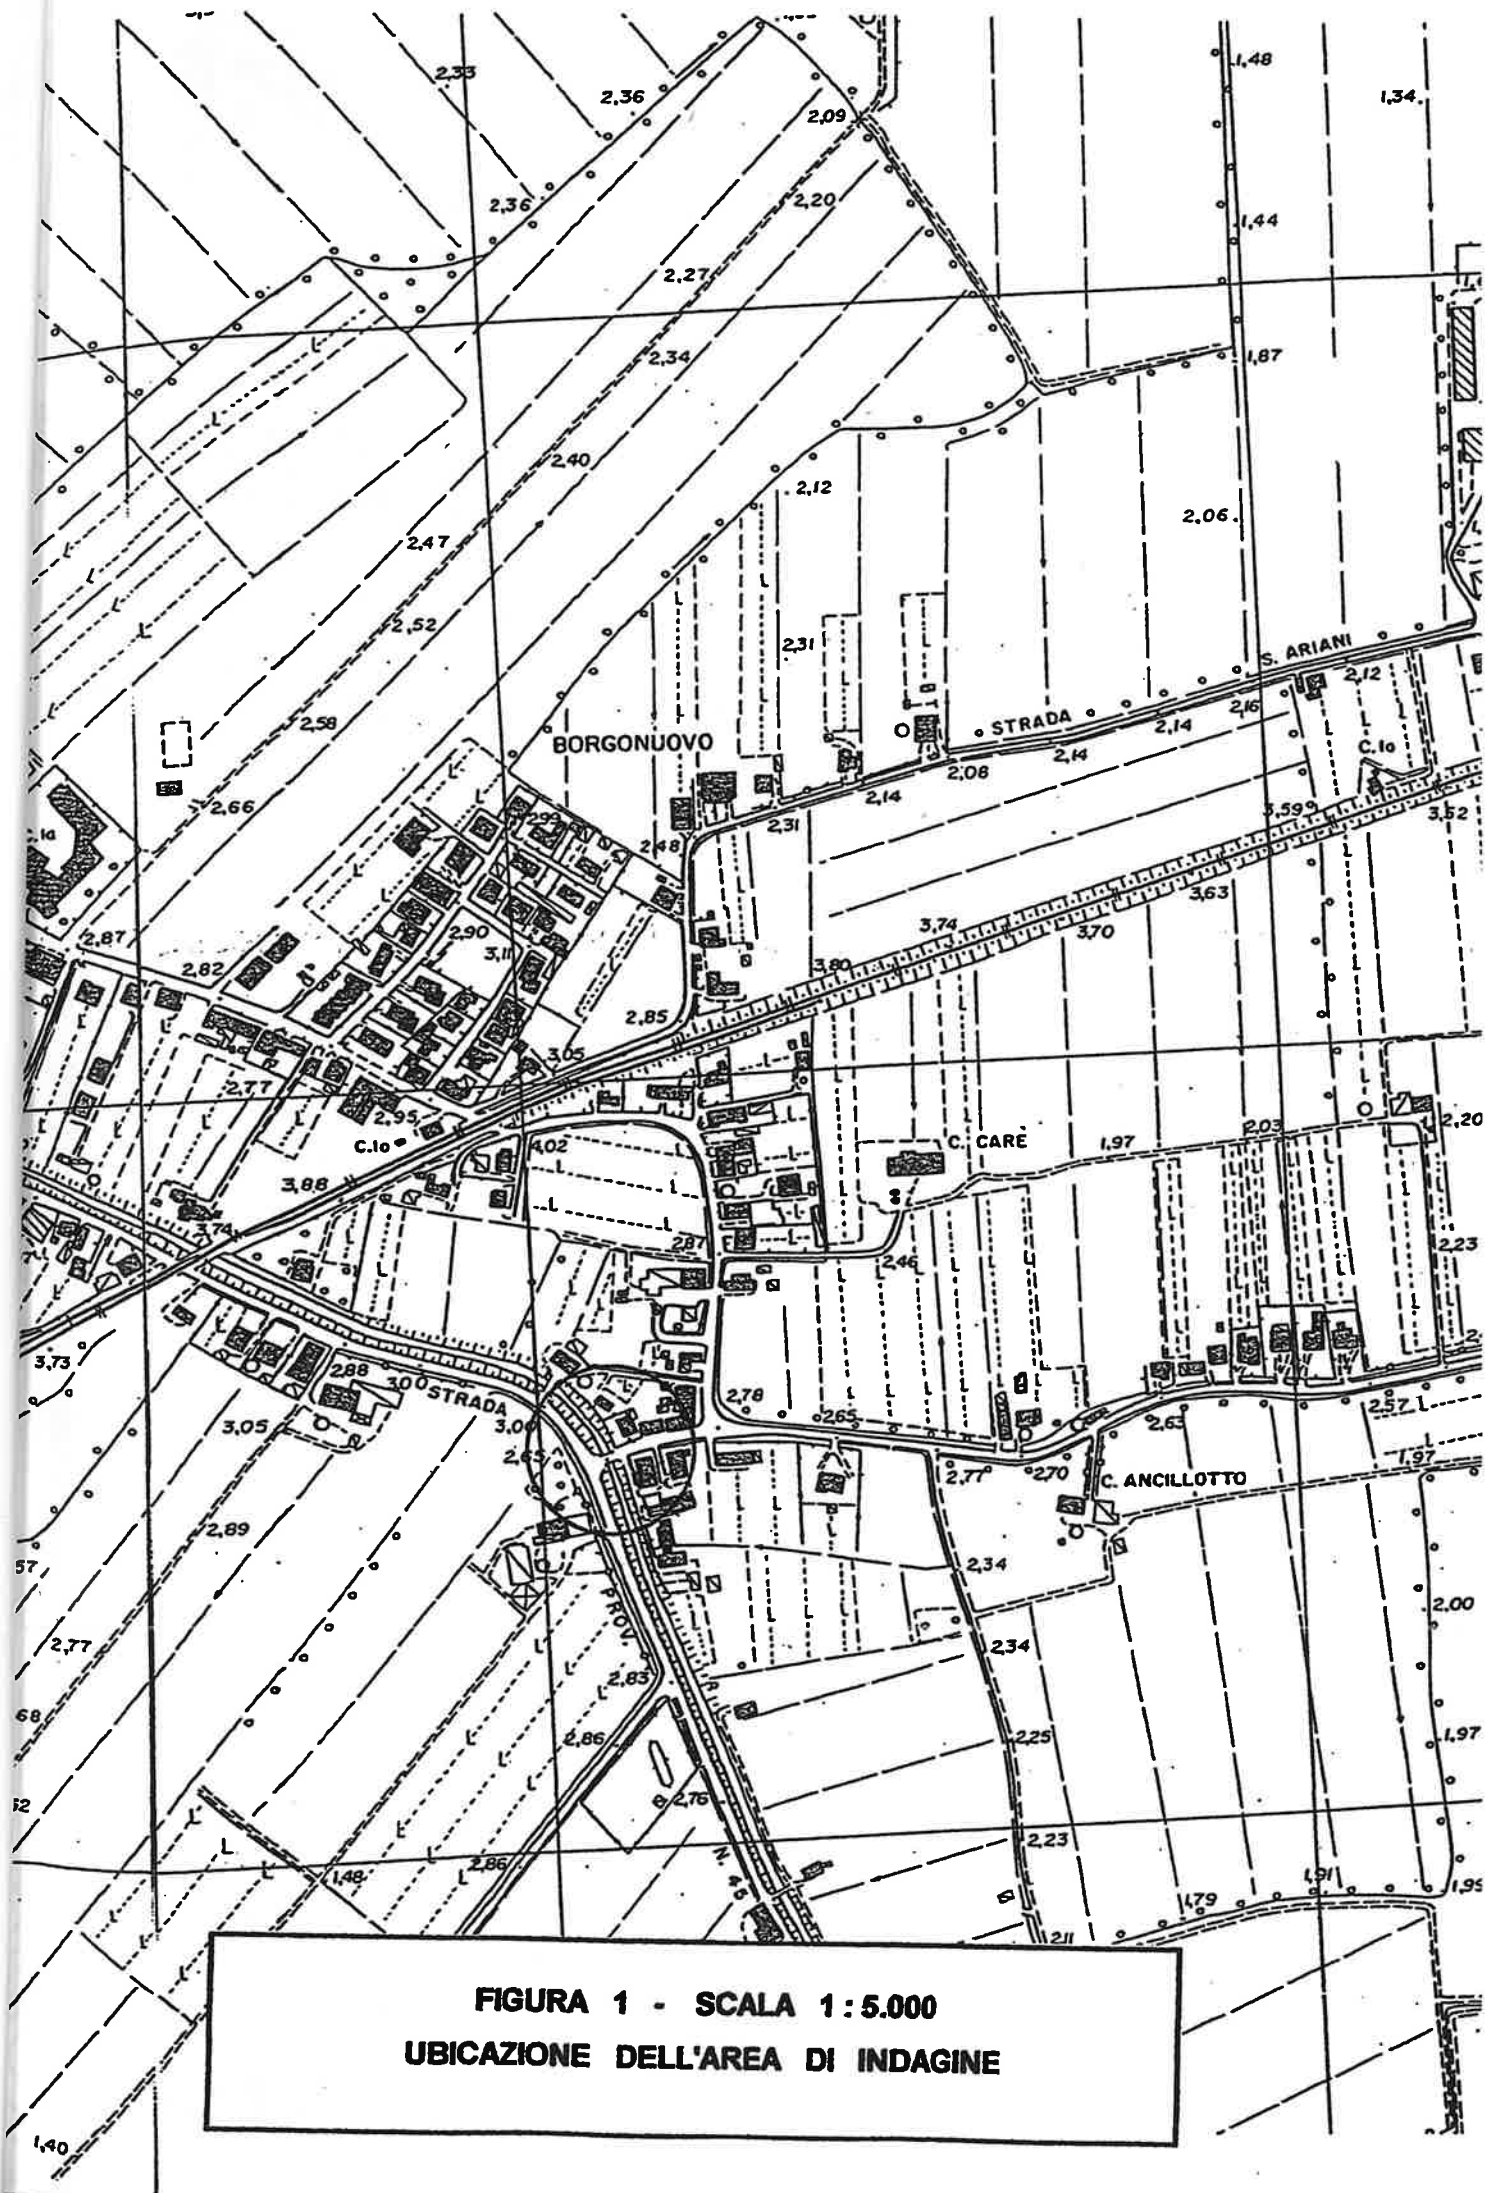


FIGURA 1 - SCALA 1:5.000
UBICAZIONE DELL'AREA DI INDAGINE

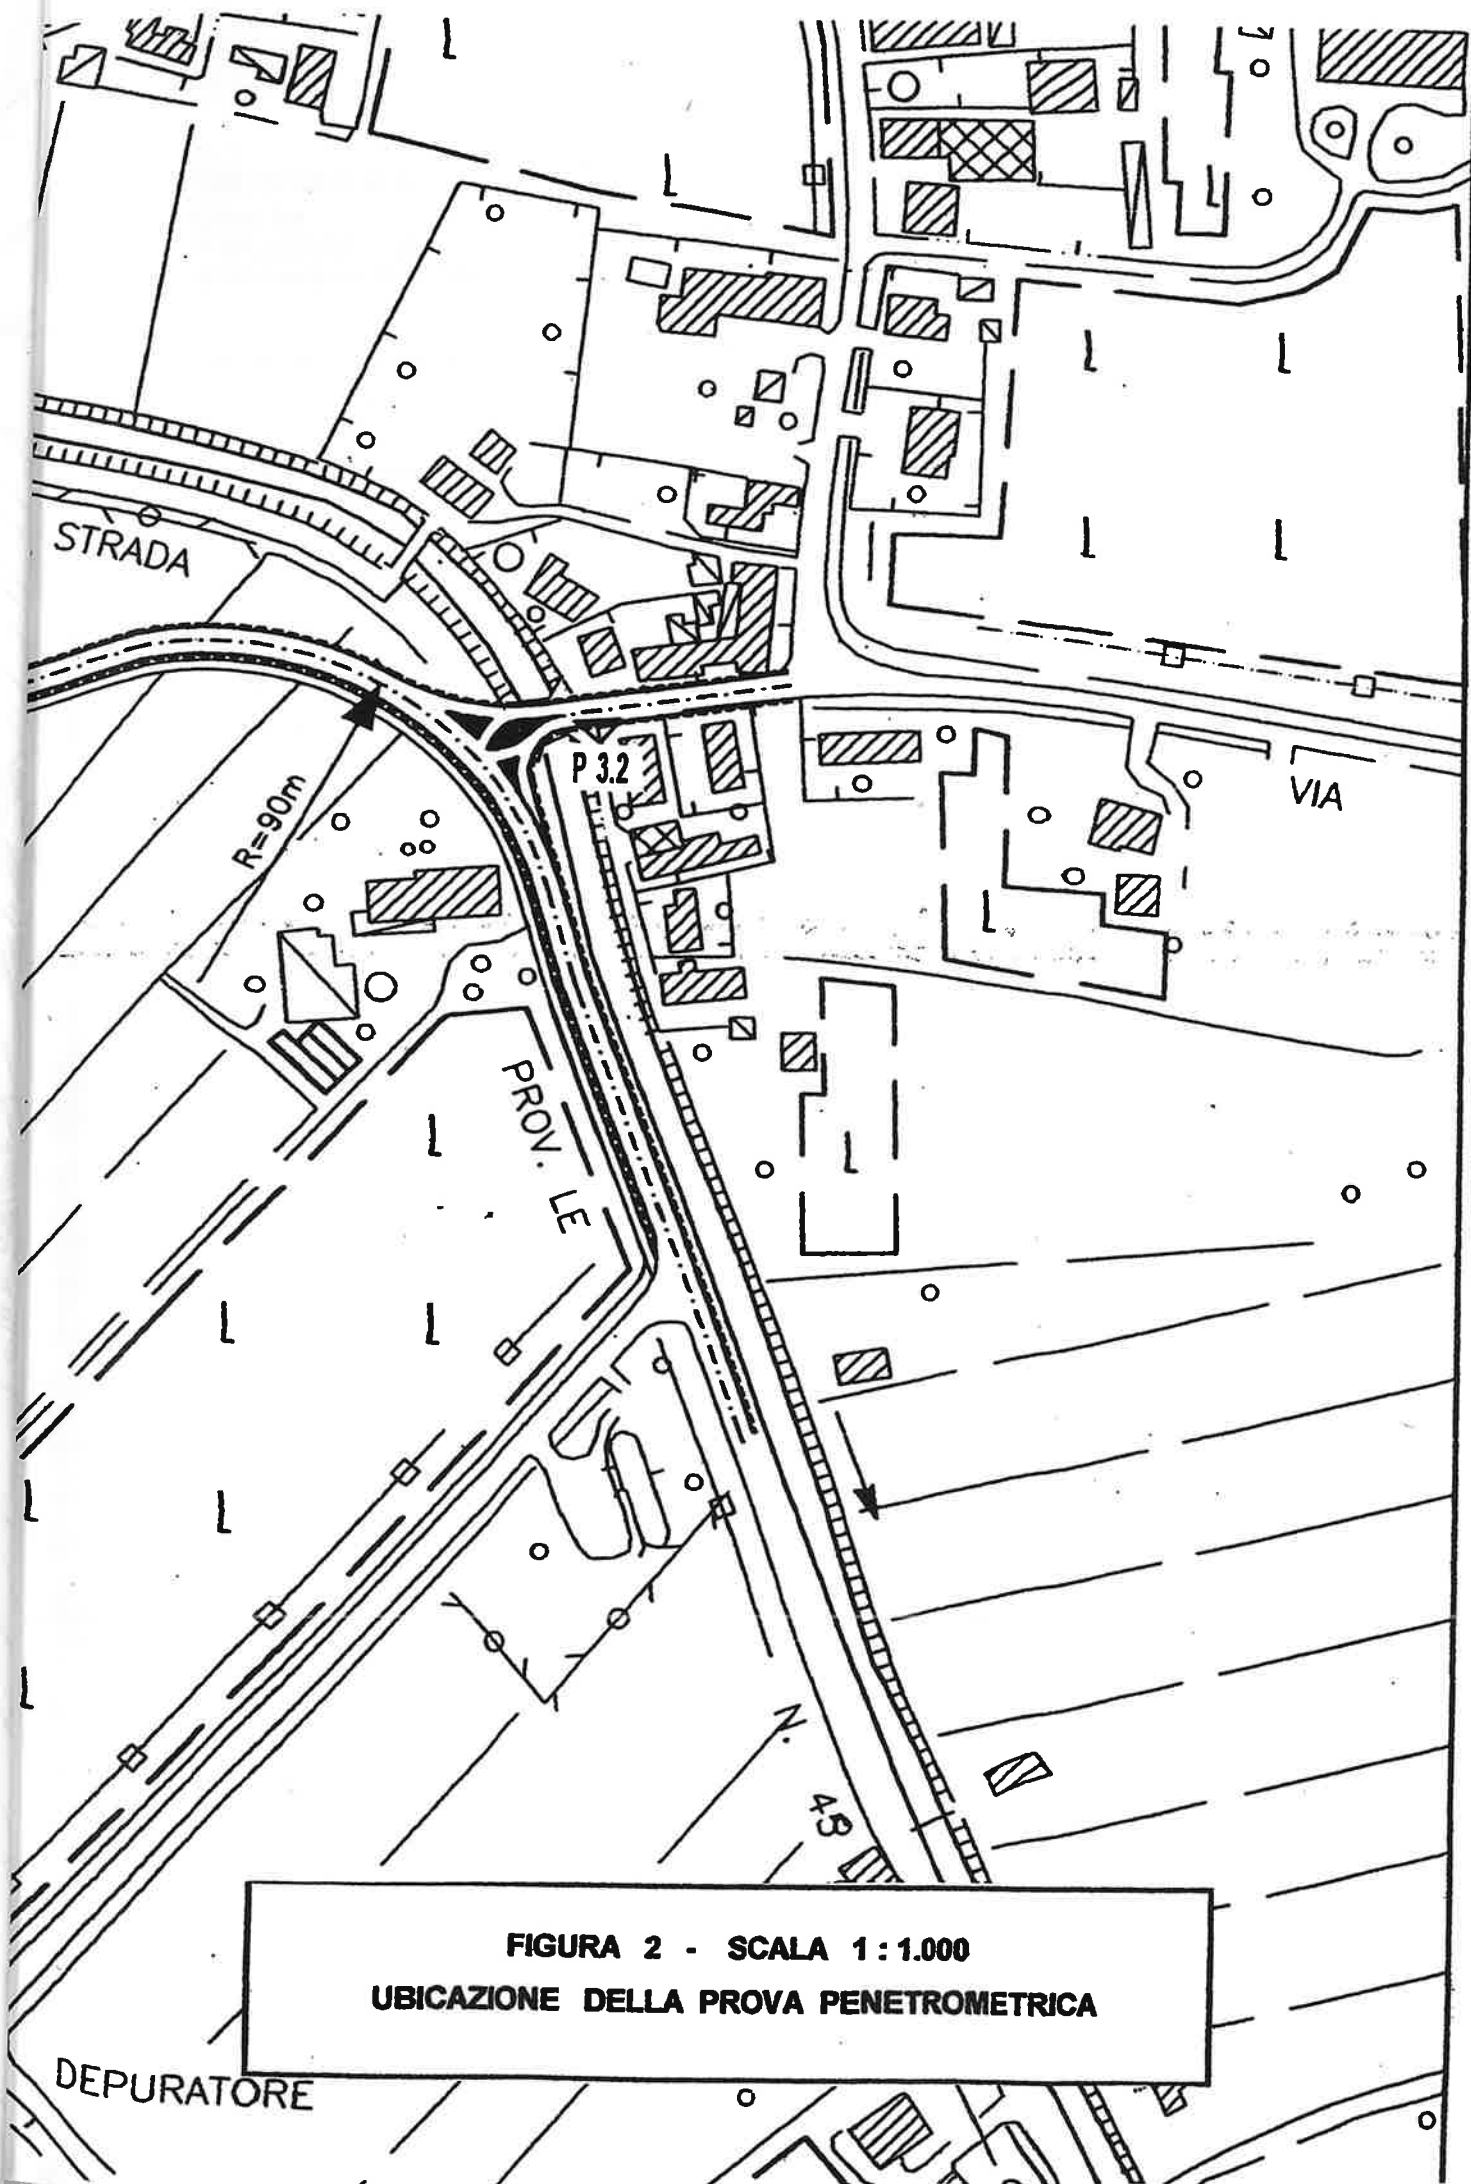


FIGURA 2 - SCALA 1:1.000
UBICAZIONE DELLA PROVA PENETROMETRICA



GEOSERVIZI S.R.L.
Via Roma, 54
31020 VILLORBA (TV)
Tel. 0422/918445 Fax 0422/918640


COMMITTENTE: DOTT. ING. FLAVIO ZANCHETTIN

CANTIERE: MEOLO


PENETROMETRIA: P3.2

DATA: 15/09/99 QUOTA: -0.40 m DA P 3.3

RAPPORTO R_p/R_1 (BEGEMANN) *

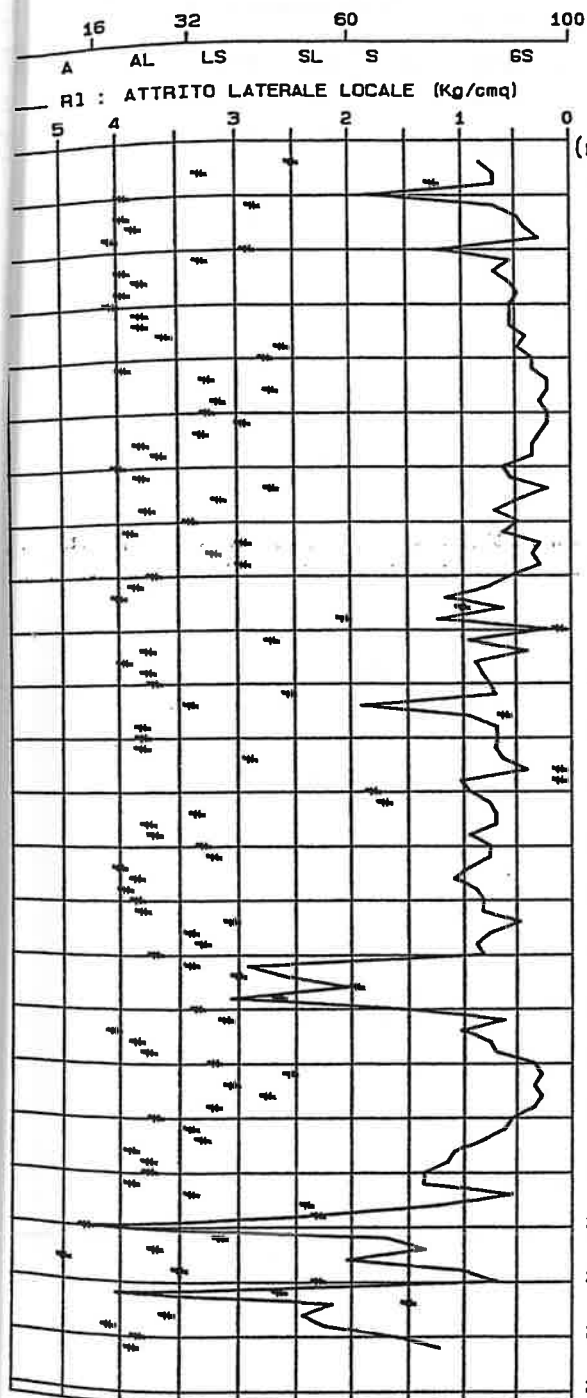

PENETROMETRO STATICO olandese da 20 tonnellate

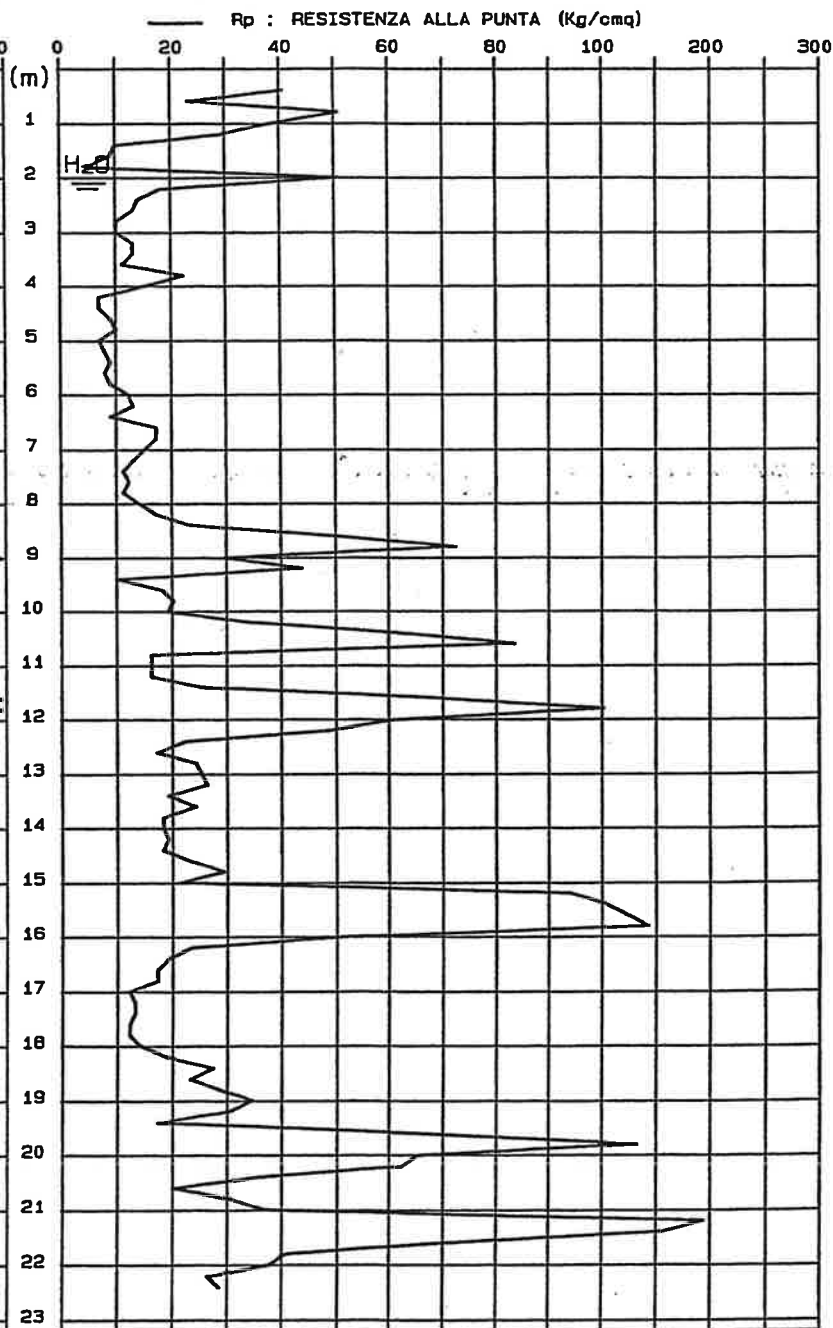

MODELLO GEOTECNICO DEL TERRENO

Penetrometria di riferimento : P3.2

Cantiere : MELO

Data : 15/09/99

Quota zero : PIANO STRADA

QUOTE DELLO STRATO (m)	SPESORE (cm)	INTERPRETAZIONE STRATIGRAFICA	Rp media (kg/cm ²)	RL media (kg/cm ²)	E' (kg/cm ²)	Phi' (gradi)	Cu (kg/cm ²)
-0.40 -1.30	90	TERRENO LINOLO SABBIOLO CON GHIAIA	36	0.94	71.35	33	0.00
-1.30 -1.90	60	ARGILLA LINOLO	8	0.38	34.77	0	0.40
-1.90 -2.30	40	LINO SABBIOLO	34	0.88	92.07	32	0.00
-2.30 -3.70	140	ARGILLA LINOLO	12	0.53	48.69	0	0.60
-3.70 -4.10	40	LINO SABBIOLO	18	0.41	56.60	29	0.00
-4.10 -6.50	240	ARGILLA LINOLO	9	0.31	37.22	0	0.45
-6.50 -8.50	200	LINO ARGILLOLO	15	0.55	57.72	0	0.75
-8.50 -9.30	80	SABBIA LINOLO	48	0.75	97.30	34	0.00
-9.30 -10.10	80	ARGILLA LINOLO	17	0.71	56.58	0	0.85
-10.10 -10.70	60	LINO SABBIOLO	59	1.18	104.93	35	0.00
-10.70 -11.30	60	ARGILLA LINOLO	16	0.67	65.20	0	0.80
-11.30 -12.30	100	SABBIA CON LINO	60	0.74	104.92	35	0.00
-12.30 -15.10	280	LINO ARGILLOLO	22	0.80	59.26	0	1.10
-15.10 -16.10	100	SABBIA LINOLO	103	2.43	193.88	38	0.00
-16.10 -18.30	220	LINO ARGILLOLO	15	0.52	60.70	0	0.75
-18.30 -19.50	120	ARGILLA CON LINO	26	1.05	54.83	0	1.30
-19.50 -19.90	40	SABBIA LINOLO	97	1.83	195.70	37	0.00
-19.90 -20.90	100	LINO ARGILLOLO	42	2.16	79.46	0	2.10
-20.90 -21.70	80	SABBIA LINOLO	113	2.34	182.98	38	0.00
-21.70 -22.40	70	ARGILLA LINOLO	34	1.70	61.19	0	1.70

Simbologia.

Rp : Resistenza alla punta (kg/cm²).

RL : Attrito laterale locale (kg/cm²).

E' : Modulo Edometrico (kg/cm²).

Phi' : Angolo d'attrito interno (gradi)