

PROF. (m)	PROVA P 5.1	PROVA P 5.1 BIS	SONDAGGIO S 5.1	FALDA (m)	SCAVO (m)
0,00	TERRENO DI RIPORTO: Sabbia e limo $R_p = 53 \text{ kg/cm}^2 - \phi = 35^\circ$ 0,50	Quota di inizio: -0,40 m da P 5.1			
1,00	Limo sabbioso $R_p = 27 \text{ kg/cm}^2 - \phi = 34^\circ$ 1,70	TERRENO DI RIPORTO: Sabbia e limo $R_p = 22 \text{ kg/cm}^2$ $c_u = 1,15 \text{ kg/cm}^2$	TERRENO DI RIPORTO: Sabbia fine	1,00	-1,60
2,00	Limo argilloso $R_p = 12 \text{ kg/cm}^2$ $c_u = 0,60 \text{ kg/cm}^2$	Limo argilloso $R_p = 12 \text{ kg/cm}^2$ $c_u = 0,60 \text{ kg/cm}^2$	Limo argilloso $R_p = 1,3 - 1,5 \text{ kg/cm}^2$ $c_u = 0,65 - 0,75 \text{ kg/cm}^2$	1,30	
3,00					
4,00	Limo sabbioso con intercalaz. argillose $R_p = 39 \text{ kg/cm}^2$ $\phi = 33^\circ$				-4,31 (-7,50 da p.f.)
5,00	Limo argilloso $R_p = 20 \text{ kg/cm}^2$ $c_u = 2,50 \text{ kg/cm}^2$	Limo sabbioso $R_p = 72 \text{ kg/cm}^2$ $\phi = 36^\circ$	Limo sabbioso $R_p = 72 \text{ kg/cm}^2$ $\phi = 36^\circ$	5,10	
6,00				5,50	5,30
7,00					
8,00	Limo sabbioso $R_p = 34 \text{ kg/cm}^2$ $\phi = 32^\circ$	Limo sabbioso $R_p = 72 \text{ kg/cm}^2$ $\phi = 36^\circ$	Limo sabbioso $R_p = 72 \text{ kg/cm}^2$ $\phi = 36^\circ$	8,30	8,00
9,00	Sabbia limosa $R_p = 150 \text{ kg/cm}^2$ $\phi = 41^\circ$	Argilla	Argilla	8,30	
10,00		Sabbia e limo $R_p = 166 \text{ kg/cm}^2$ $\phi = 41^\circ$	Limo sabbioso	9,00	
11,00			Sabbia limosa		

Limo argilloso con intercalaz. sabbiose $R_p = 27 \text{ kg/cm}^2$ $c_u = 1,35 \text{ kg/cm}^2$	10,50				
Limo sabbioso con intercalaz. argillose $R_p = 98 \text{ kg/cm}^2$ $\phi = 38^\circ$	10,70	10,70			
Sabbia limosa $R_p = 150 \text{ kg/cm}^2$ $\phi = 41^\circ$	12,50				
	13,50	13,10	13,10		
Sabbia limosa con intercalaz. argillose $\phi = 36^\circ$	15,30				
Limo e sabbia $R_p = 80 \text{ kg/cm}^2$ $\phi = 36^\circ$	15,10	15,10			
Limo e sabbia $R_p = 80 \text{ kg/cm}^2 - \phi = 36^\circ$ 17,90			18,00		

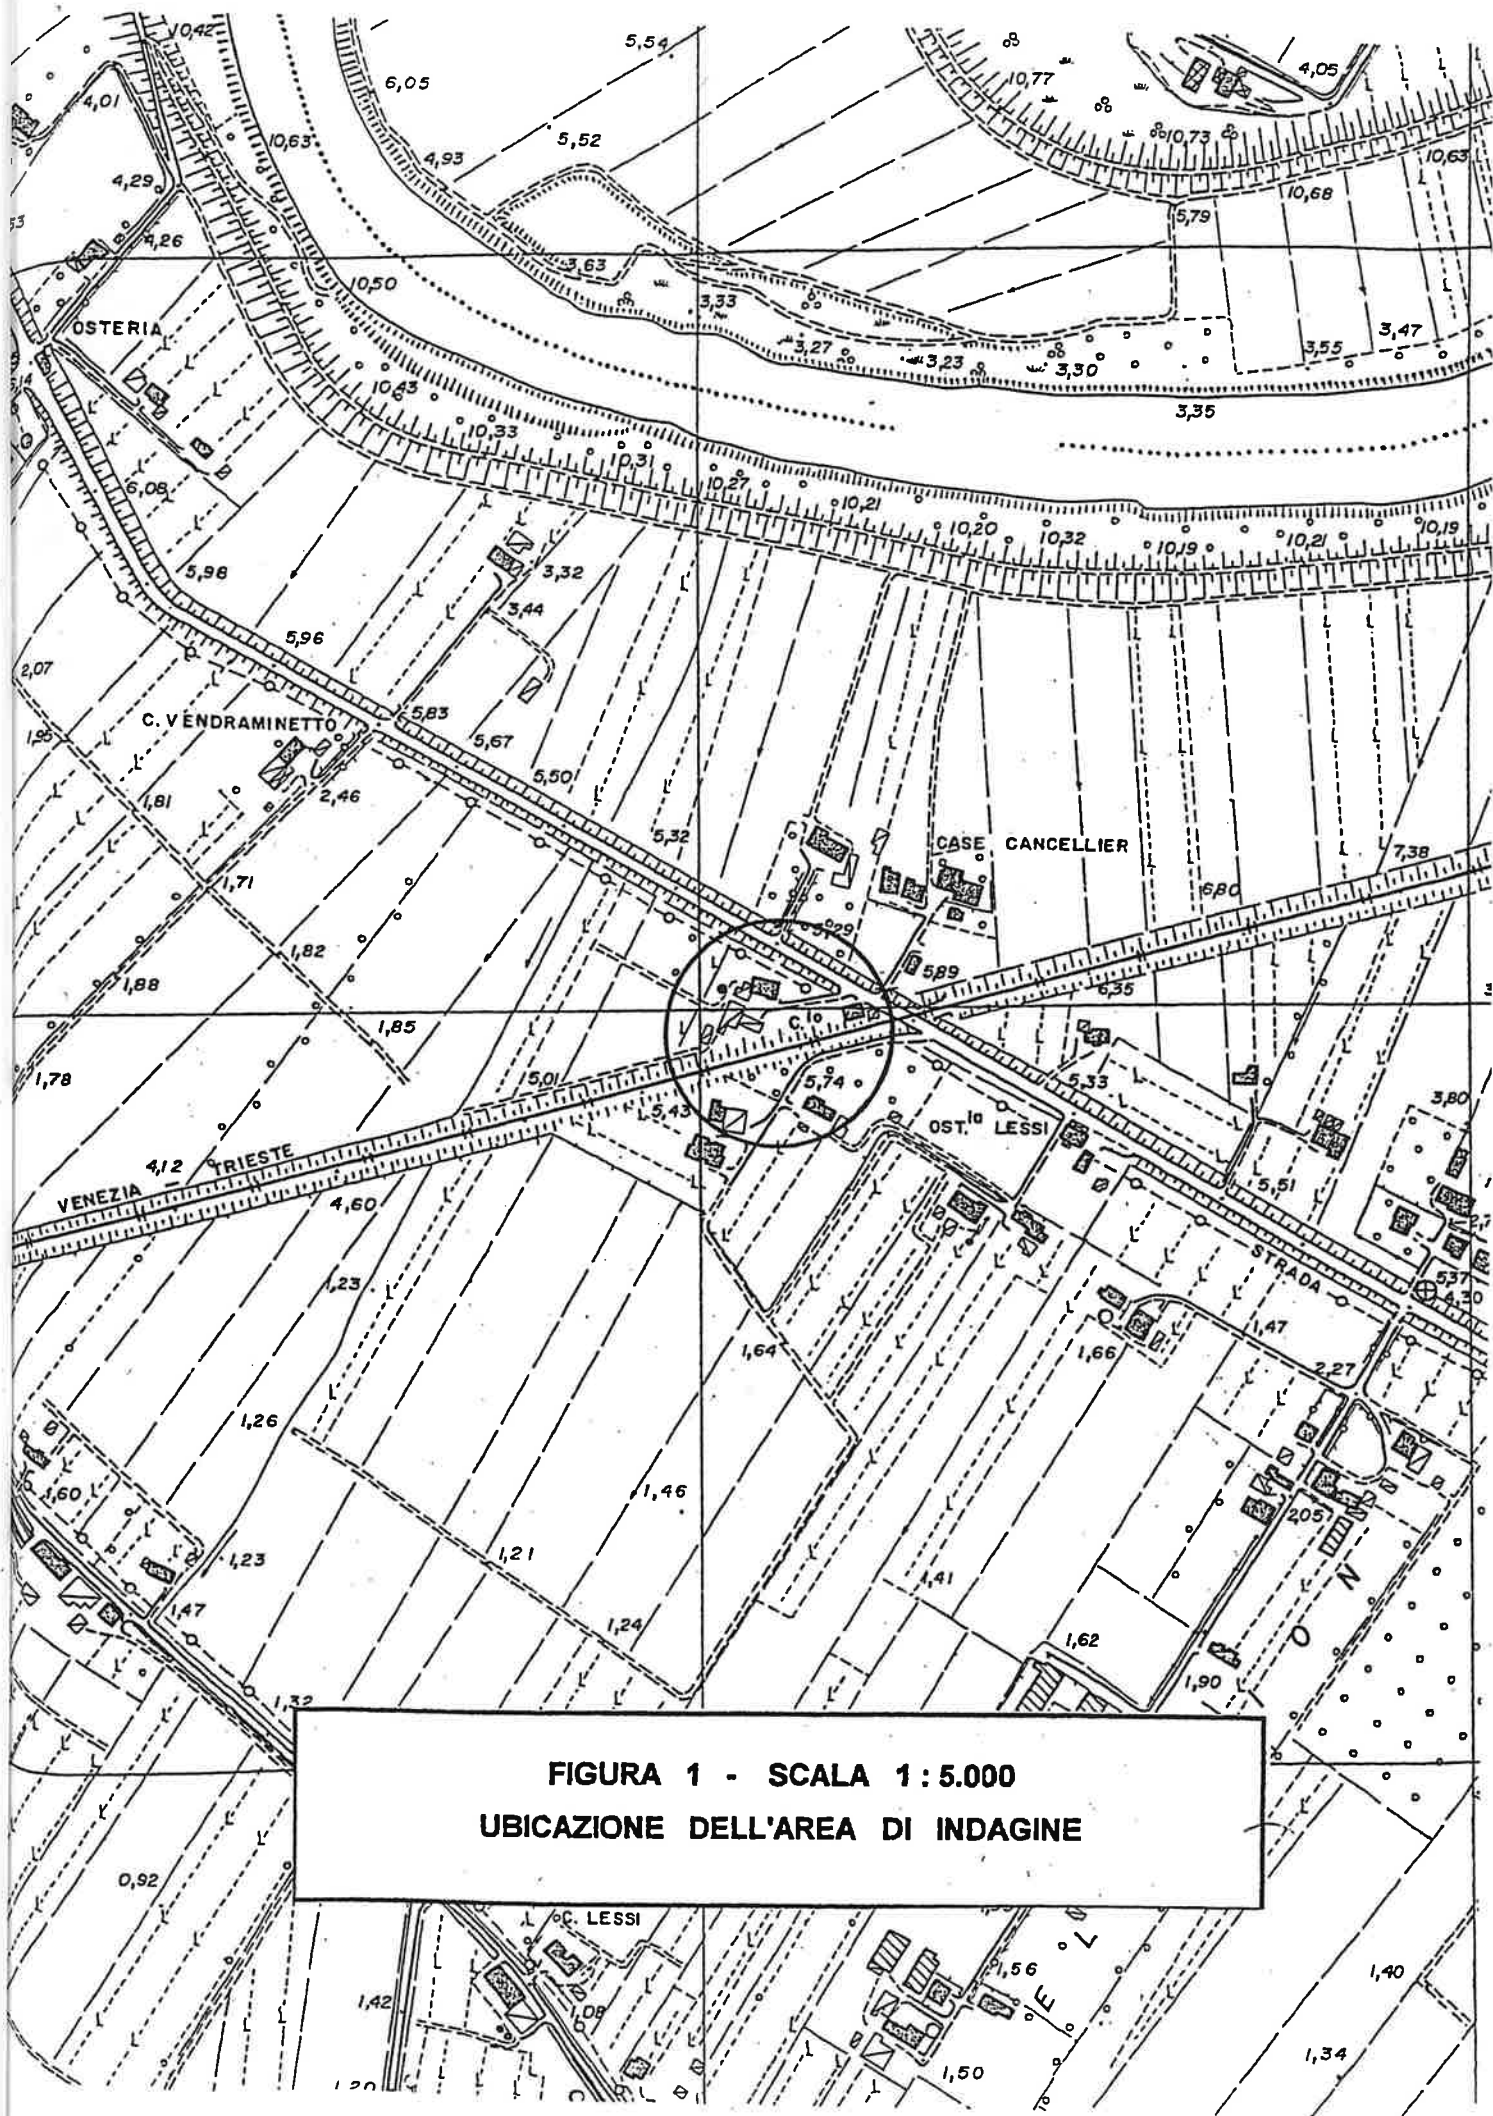


FIGURA 1 - SCALA 1:5.000
UBICAZIONE DELL'AREA DI INDAGINE


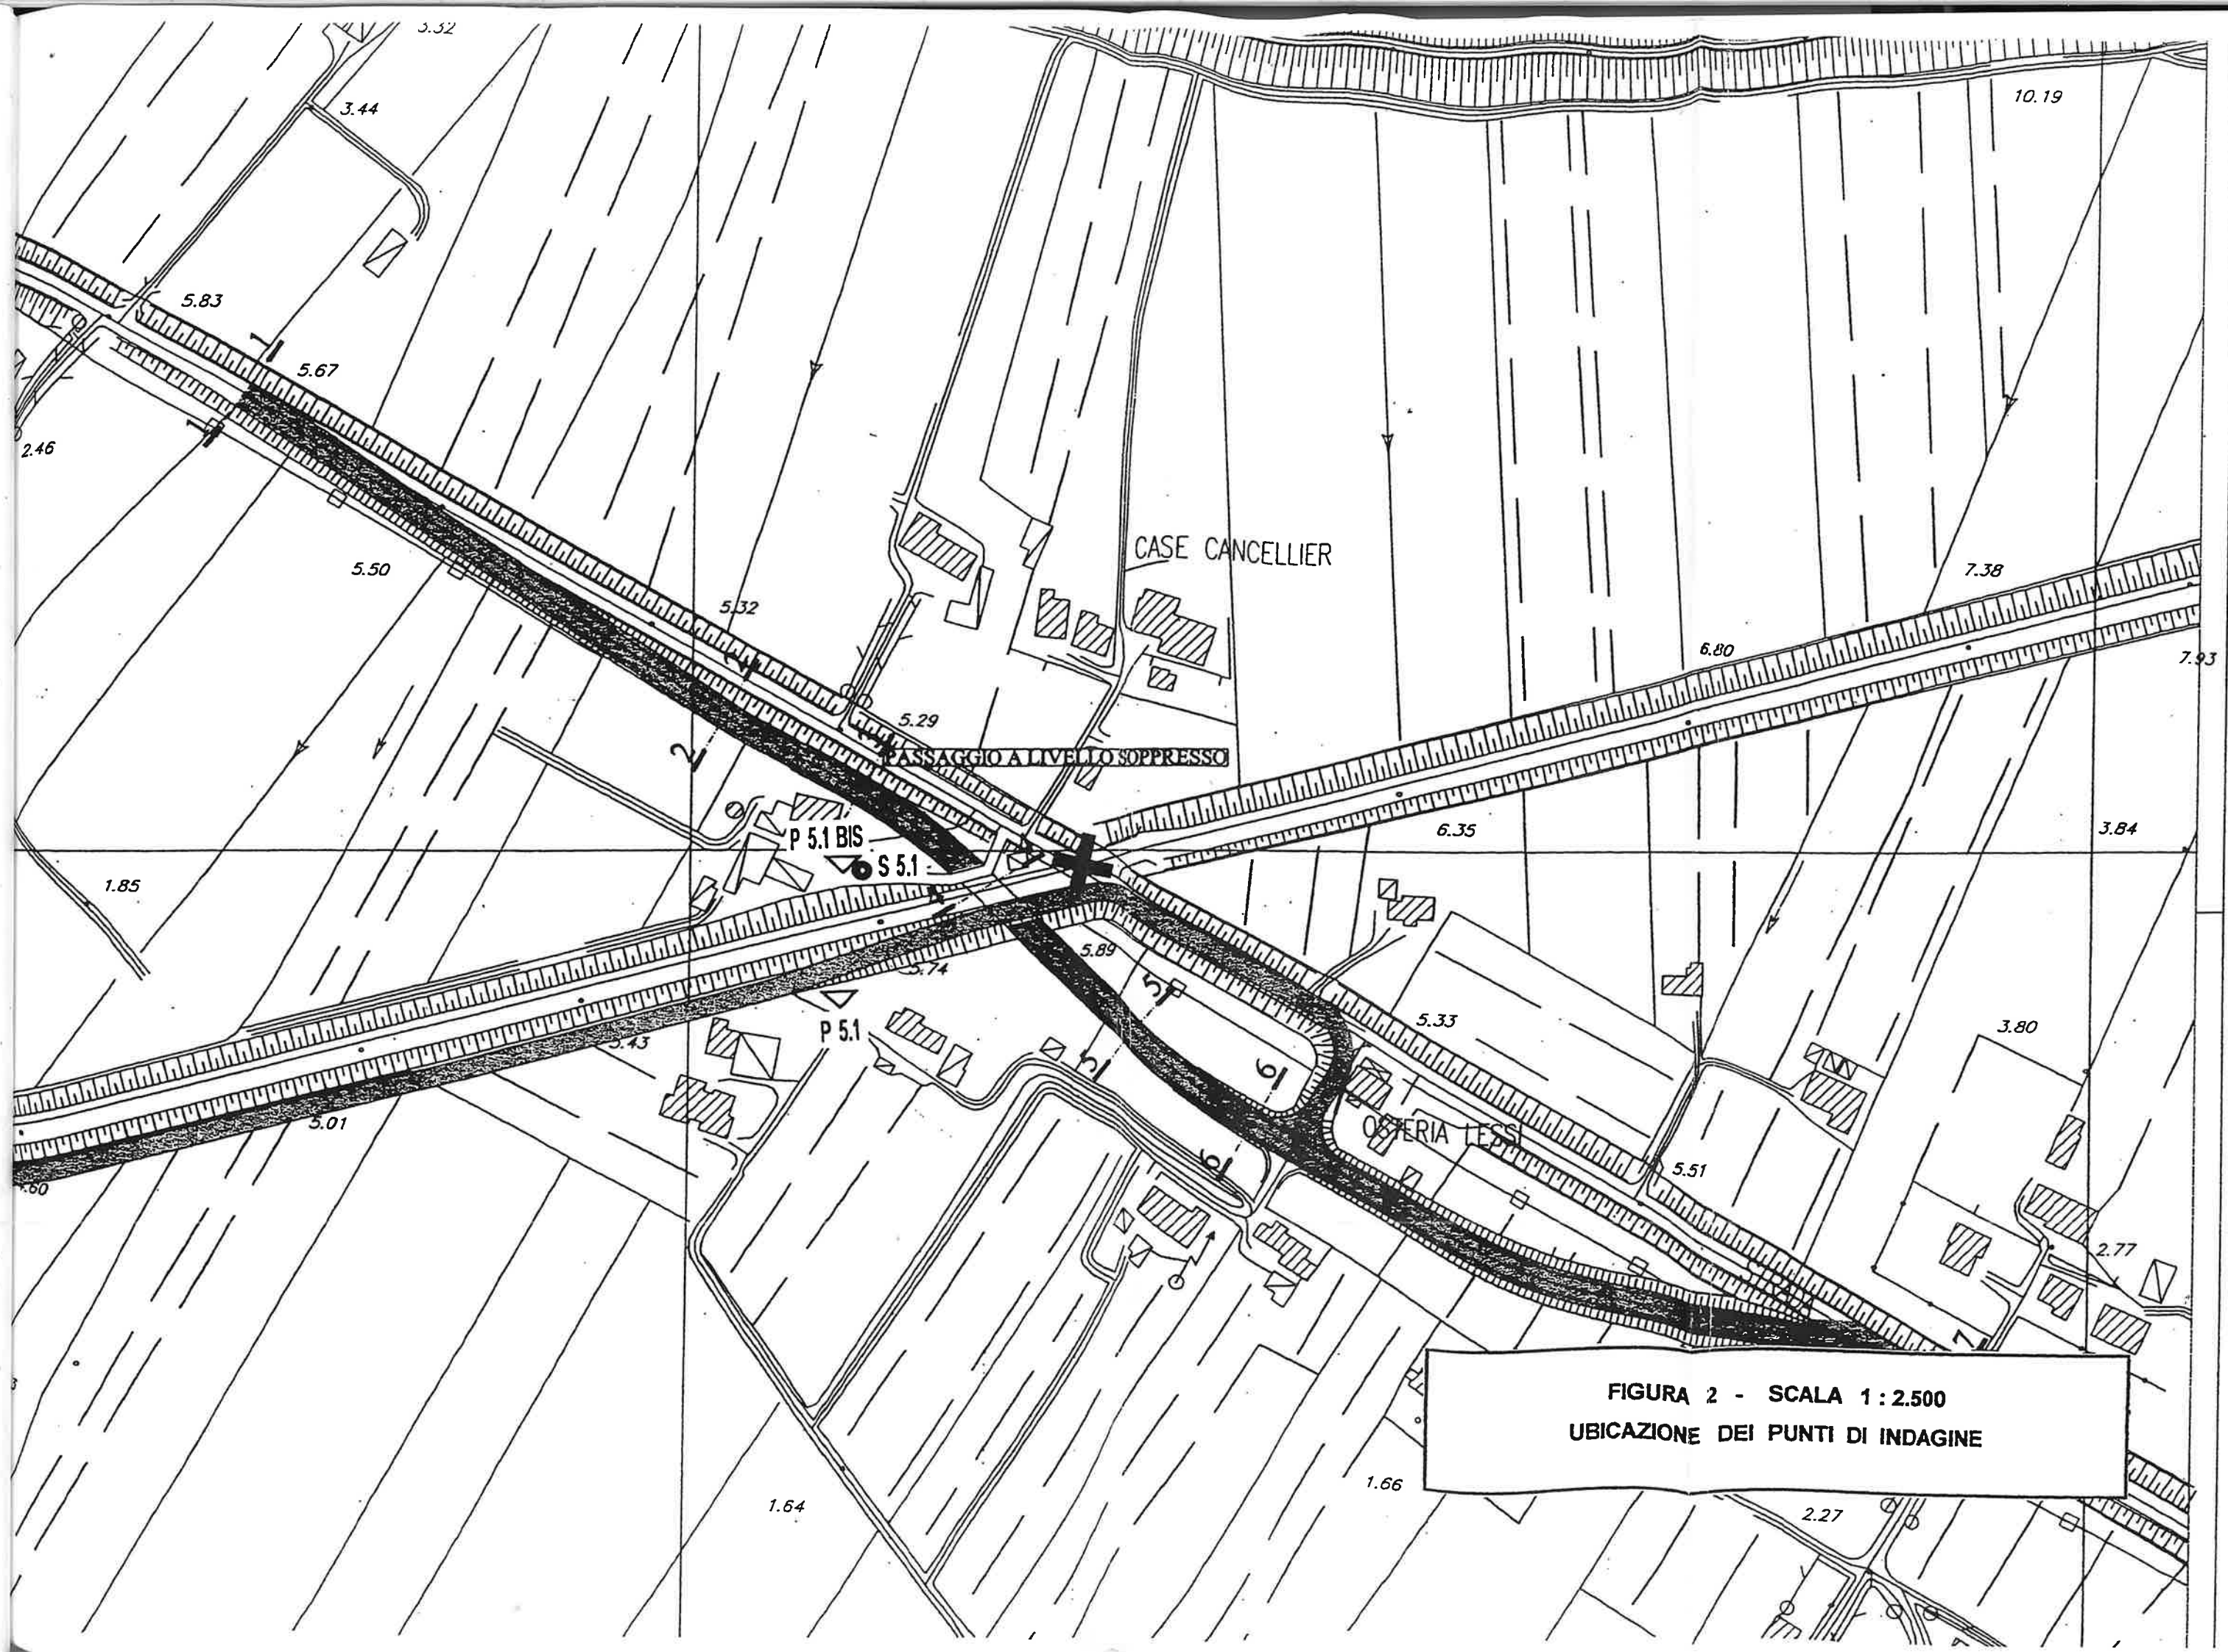


FIGURA 2 - SCALA 1:2.500
UBICAZIONE DEI PUNTI DI INDAGINE

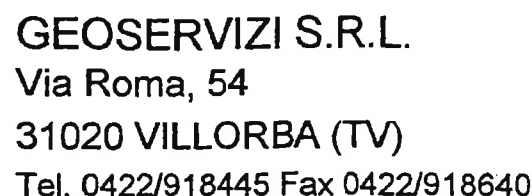

CANTIERE: MUSILE DI PIAVE - ARGINE S. MARCO

QUOTA INIZIO: - 3.59 DA P. FERRO

ASSISTENTE: DOTT. GEOL. C. GALLI

OPERATORE: SIG. A. FERRARETTO

PERFORATRICE: ATLAS COPCO A 30 T

SONDAGGIO

S 5.1

MUSILE DI PIAVE -
ARGINE S. MARCO

CAMPIONI RIMANEGGIATI

☐ da carotiere semplice

● da S.P.T.

CAMPIONI INDISTURBATI

☐ con Shelby Tube

■ con Osterberg

OSSERVAZIONI:

Materiale riposto in n. 4 cassette catalogatrici e fotografato.
Eseguita n. 1 prova di permeabilità Lefranc a carico variabile a 5 m.

[illegible]